


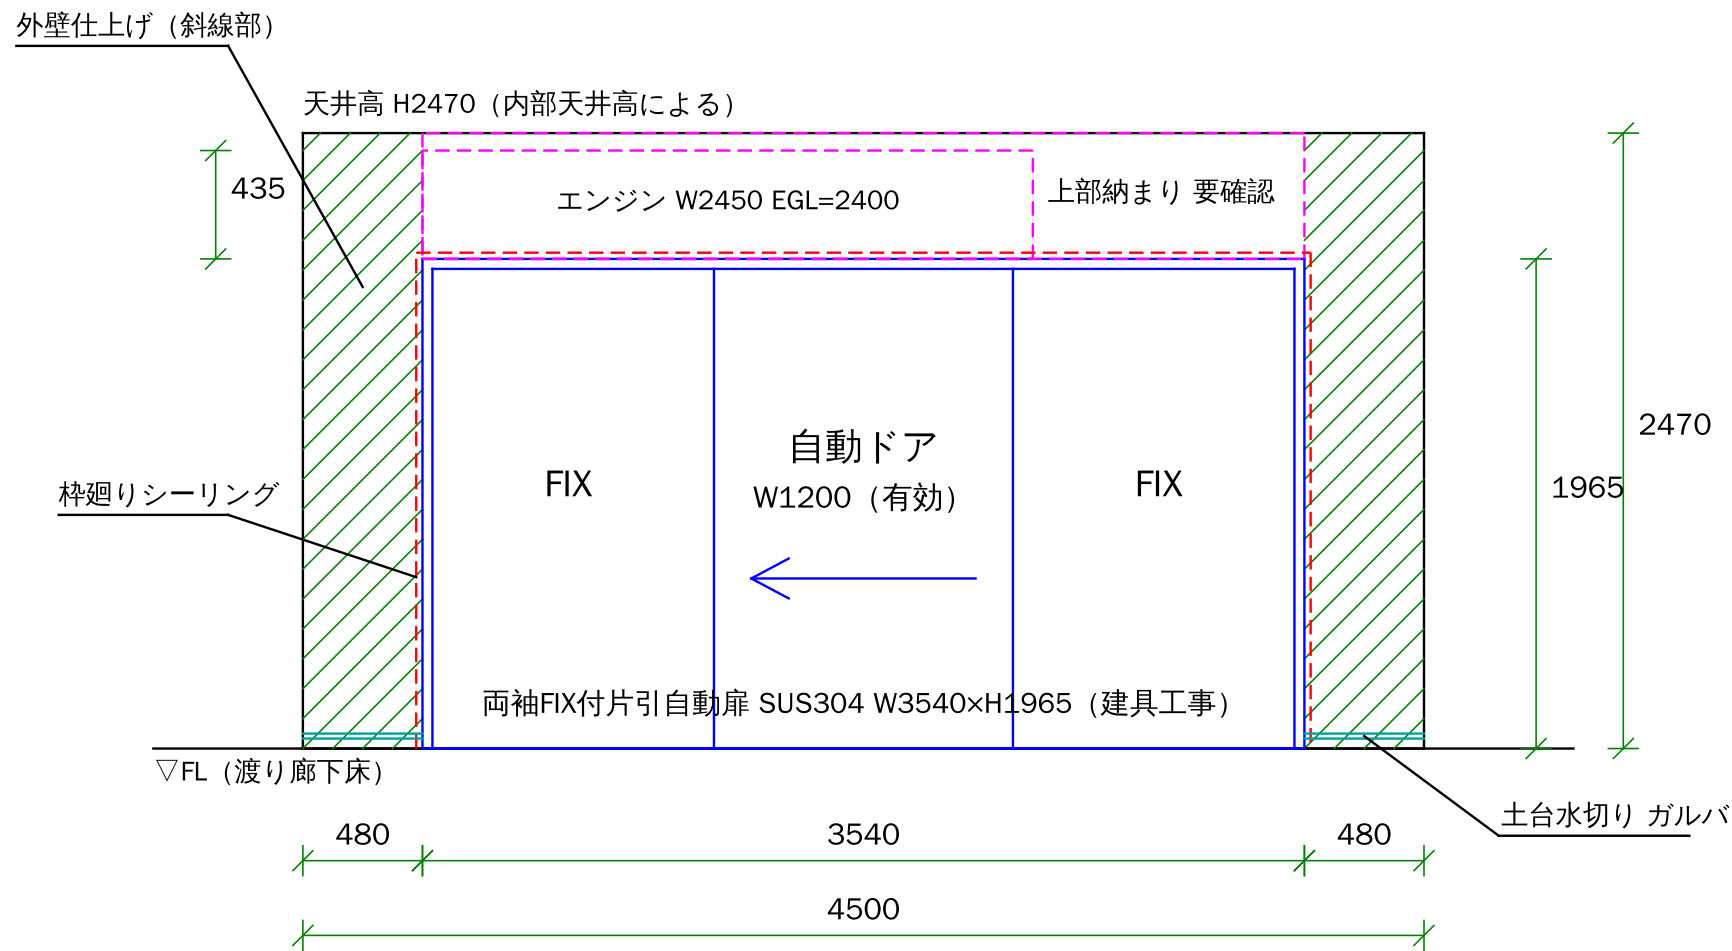

外部展開図 (自動ドア面) S=1/30

【外壁仕上げ】

- ・斜線部：透湿防水シート + 波形ラス + モルタル塗り (下・中塗り) + 吹付塗装
0.48m×2.47m×2箇所 ≒ 2.4㎡
- ・土台水切り：ガルバリウム鋼板 L≒1.0m
- ・枠廻りシーリング：変成シリコン L≒7.5m

【注記】

- ・全体幅4500は計画平面図 (4535) による概寸
- ・建具寸法は建具見積 (W3540×H1965) による
- ・建具位置は中央振分け (両袖480) と仮定
- ・上部 (H1965～) の納まりは建具業者と要確認
- ・仕上げ仕様は既存外壁に合わせ現地確認のこと