


南面

アサヒエンジニアリング様

※庇が無い為紫外線の被害が著しい。ビート（引き違い）シール（FIX）共に硝子廻り打替えをおすすめします。

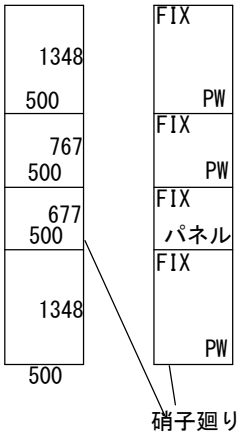


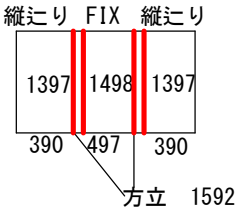

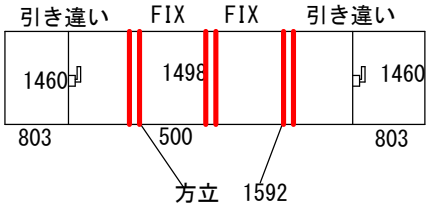


東面

※隣の建物が日よけになっている為ビートは被害無し。　2階FIXは硝子廻り打替えをおすすめします。

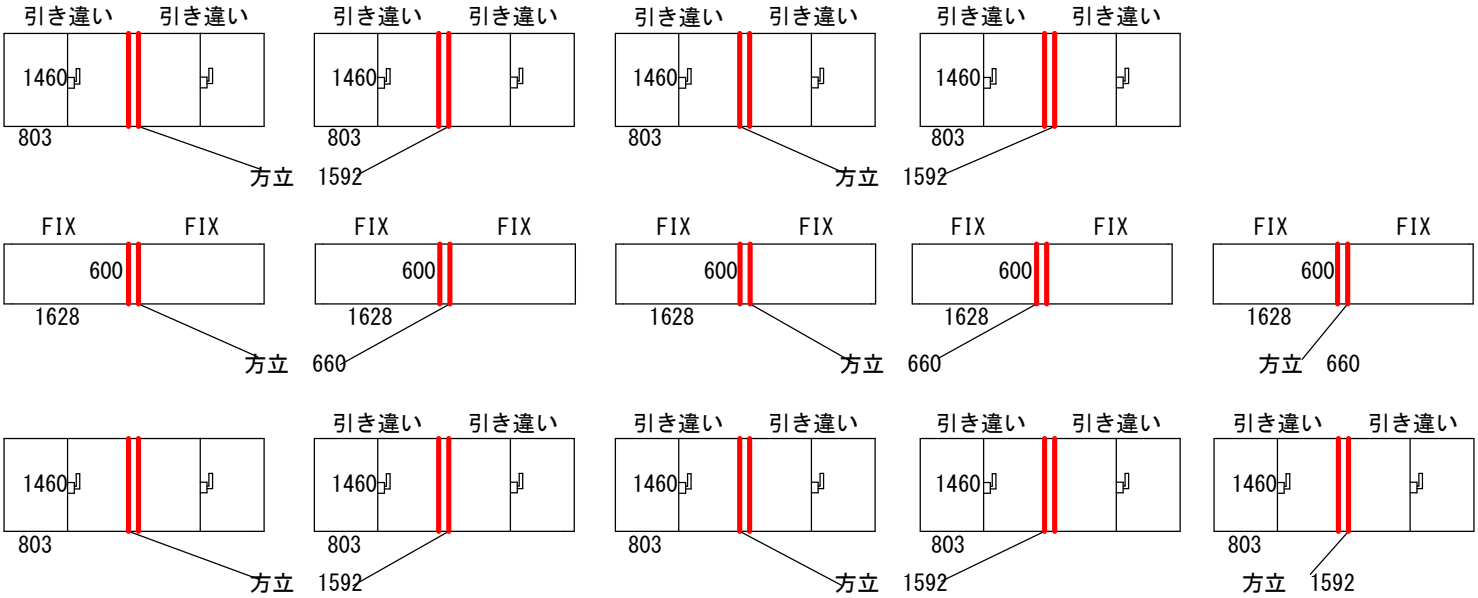

西面

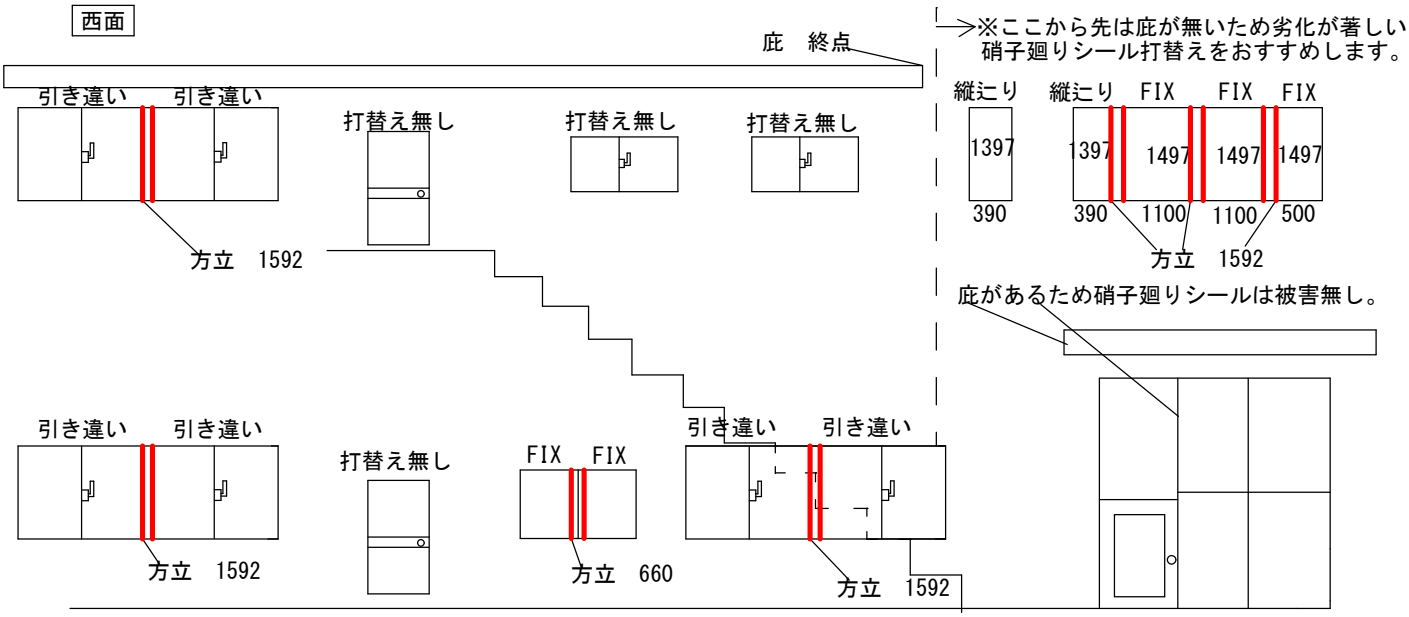

株式会社アイビ建築