


本願寺様 嘉枝堂渡り廊下 スロープ部パース（東から西を見る）

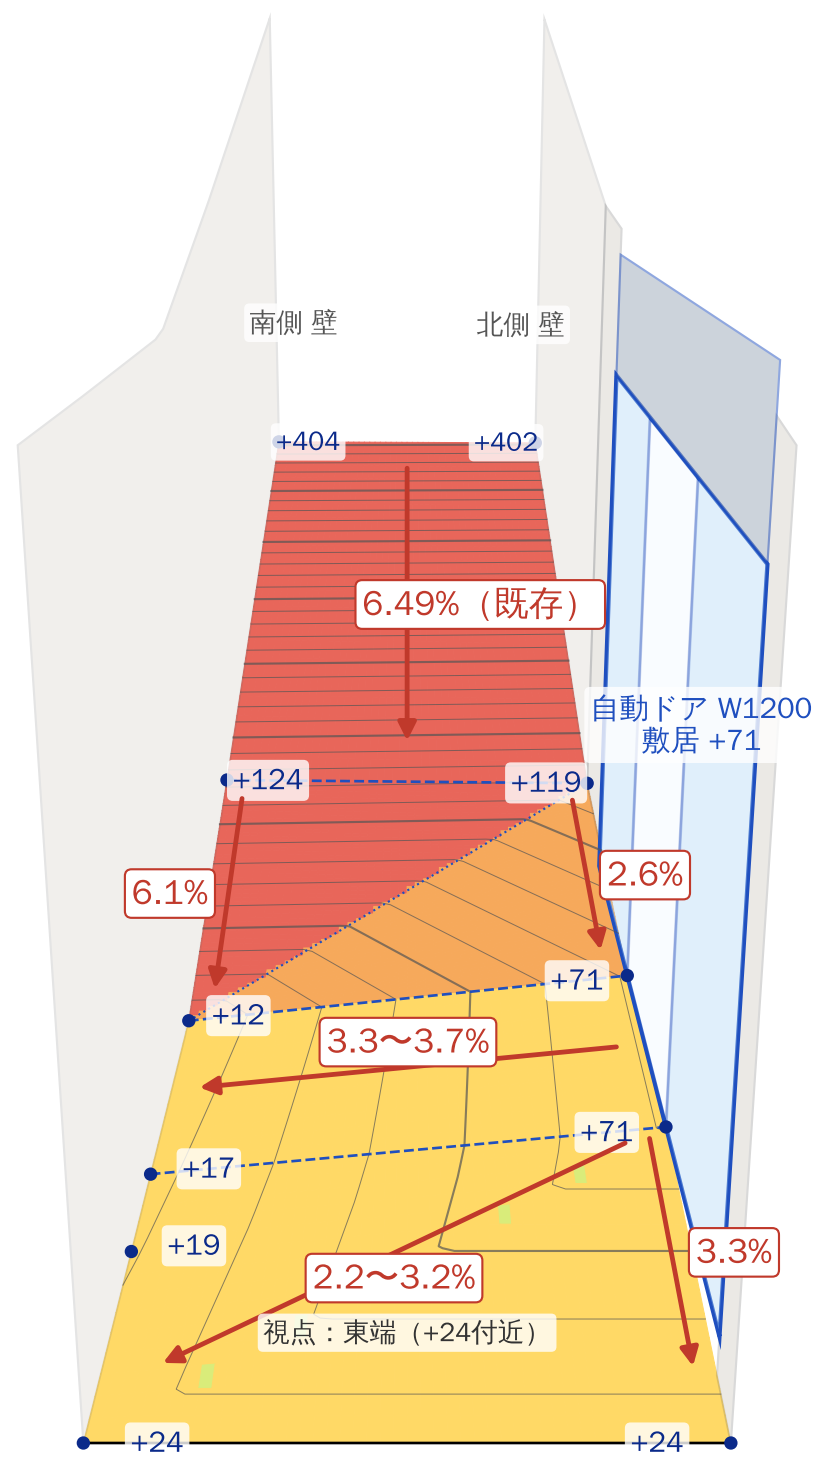

床の勾配（色分け）

2%未満
2～3%
3～4%
4～5%
5%以上

- ・ 数字は計画高さ（mm、±0基準）
 - ・ 赤矢印は下り方向と勾配
 - ・ 細線は高さ10mmごとの等高線
 - ・ 扉前（ドア幅部分）は幅方向に
扉側+71 → 南壁側+12～+17
（3.3～3.7%）の片流れ
 - ・ 6.1%（南壁側の縦断）は計画高さ
+12→+124 から算出した値
- ※高さ方向を3倍に強調して表示
※計画平面図（2026/09/15）より作成
した概略パースです

